


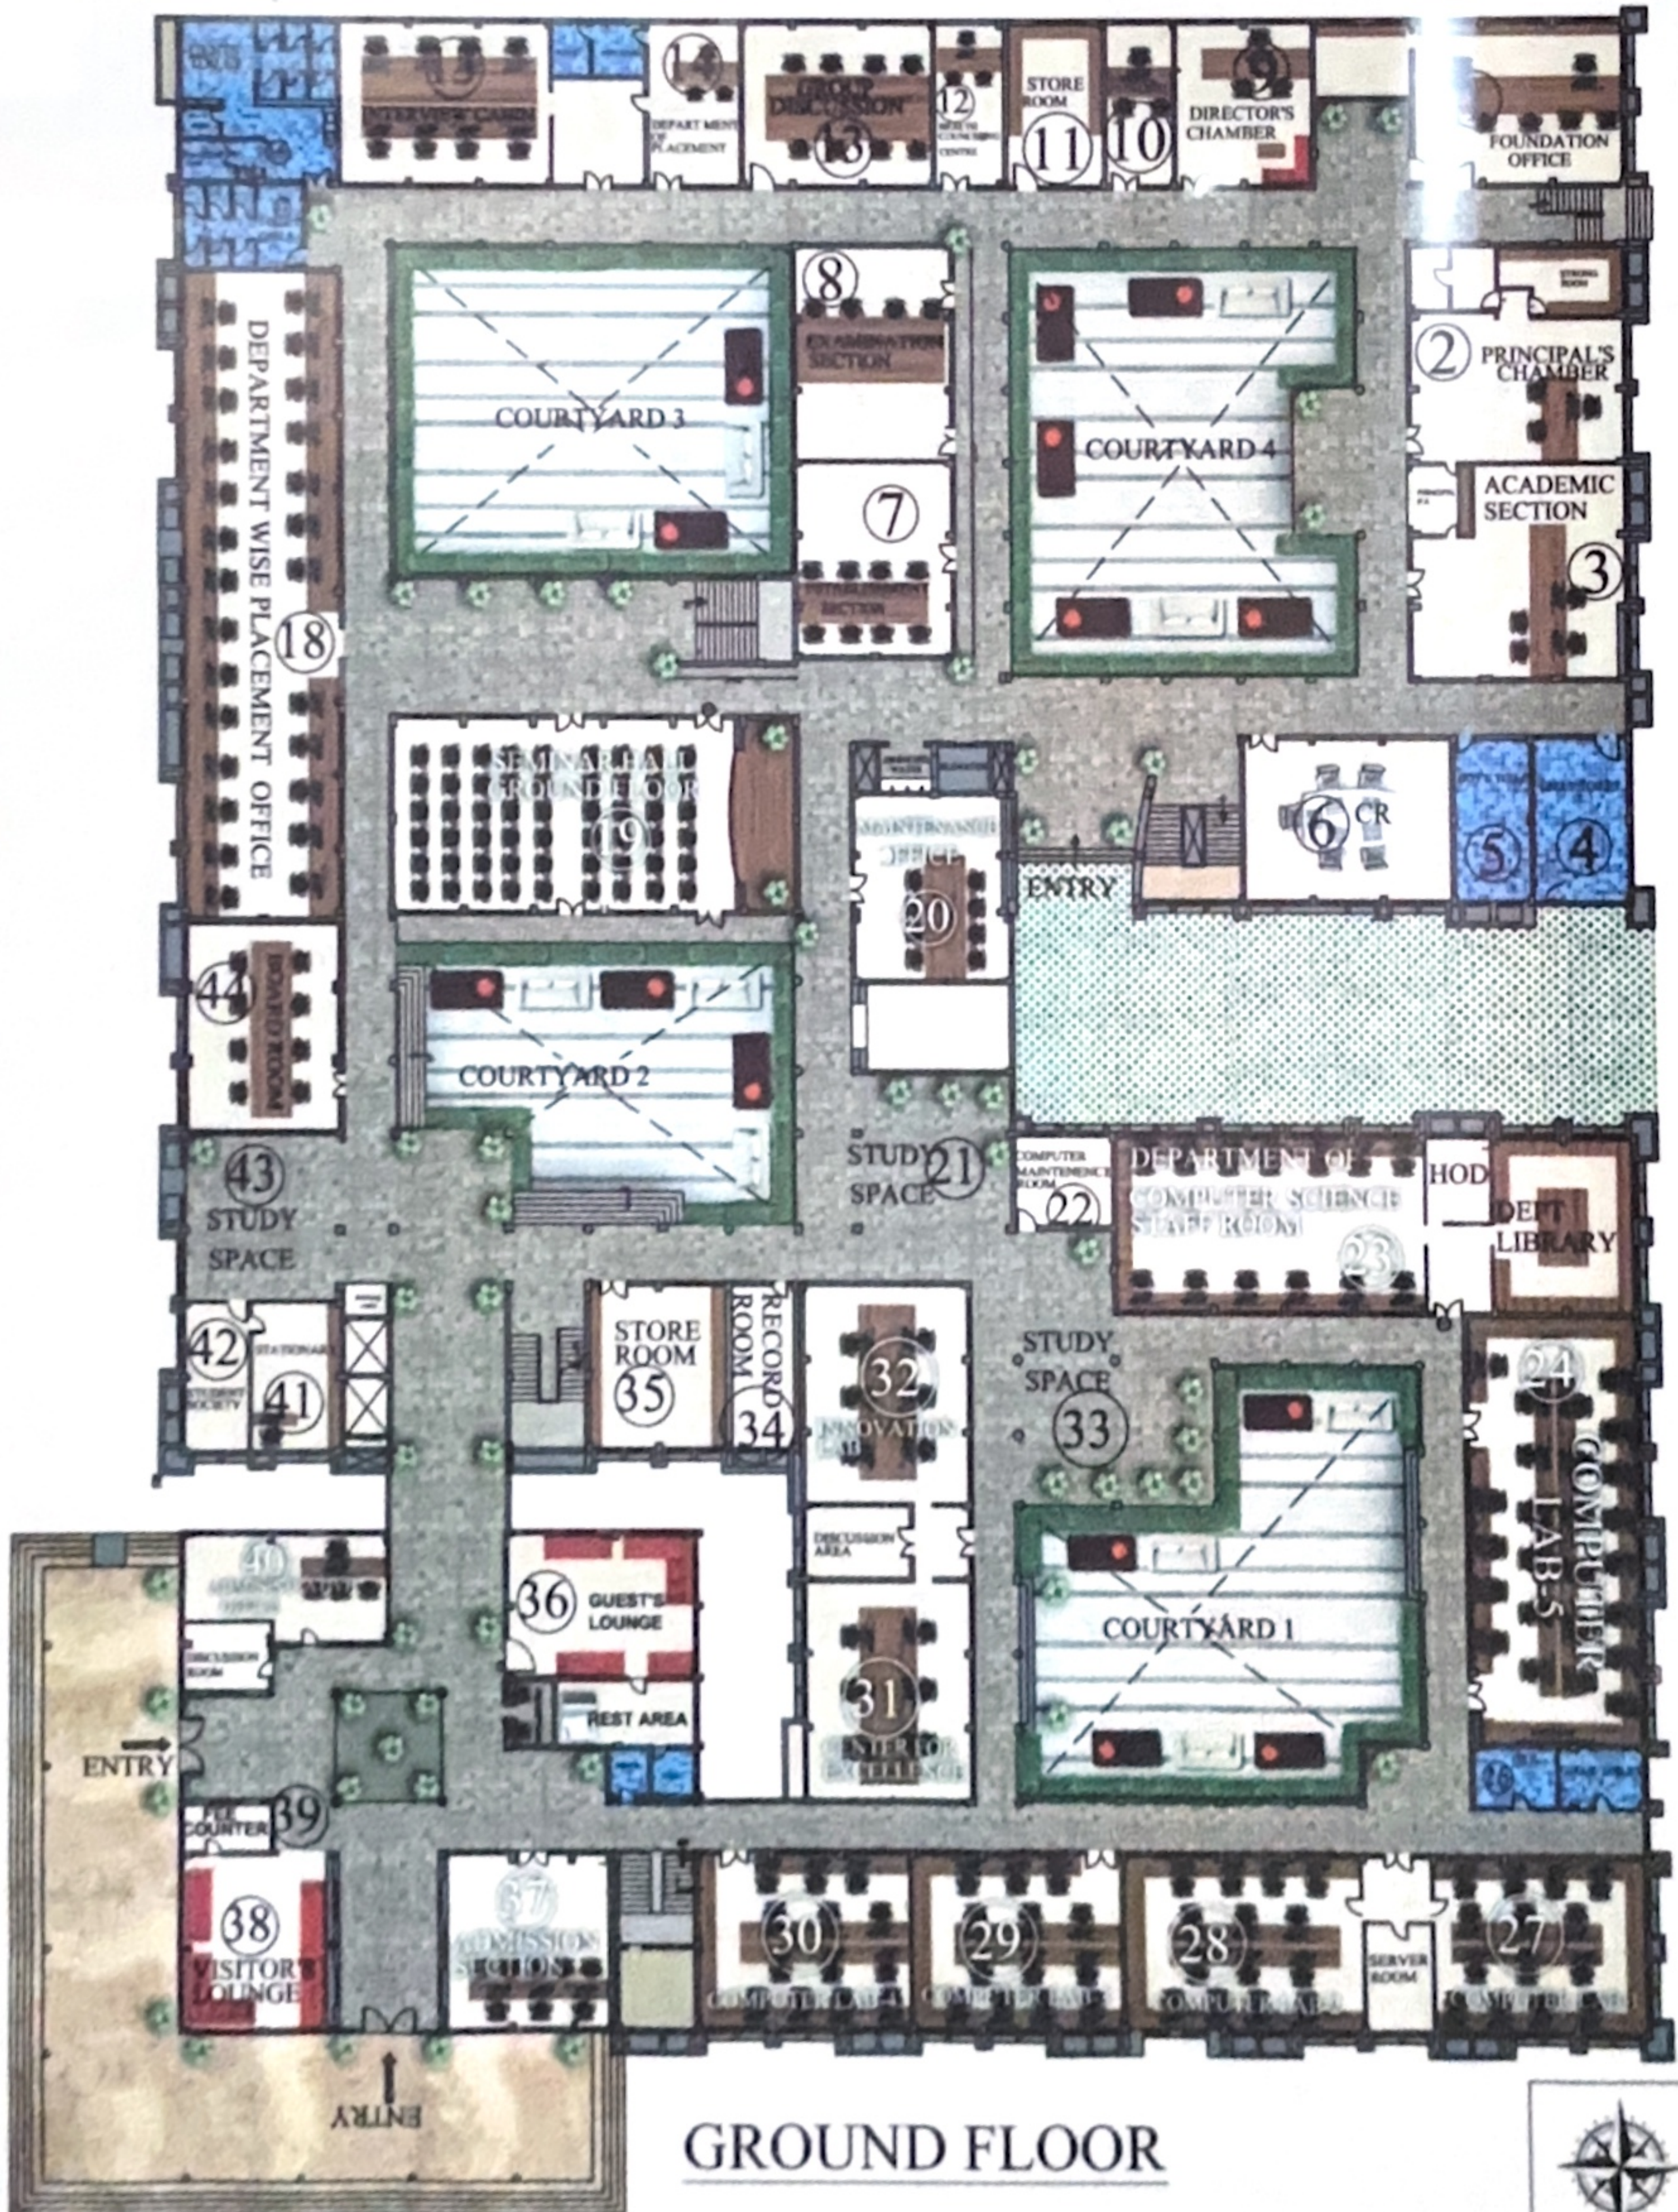


WORKSHOP GROUND FLOOR

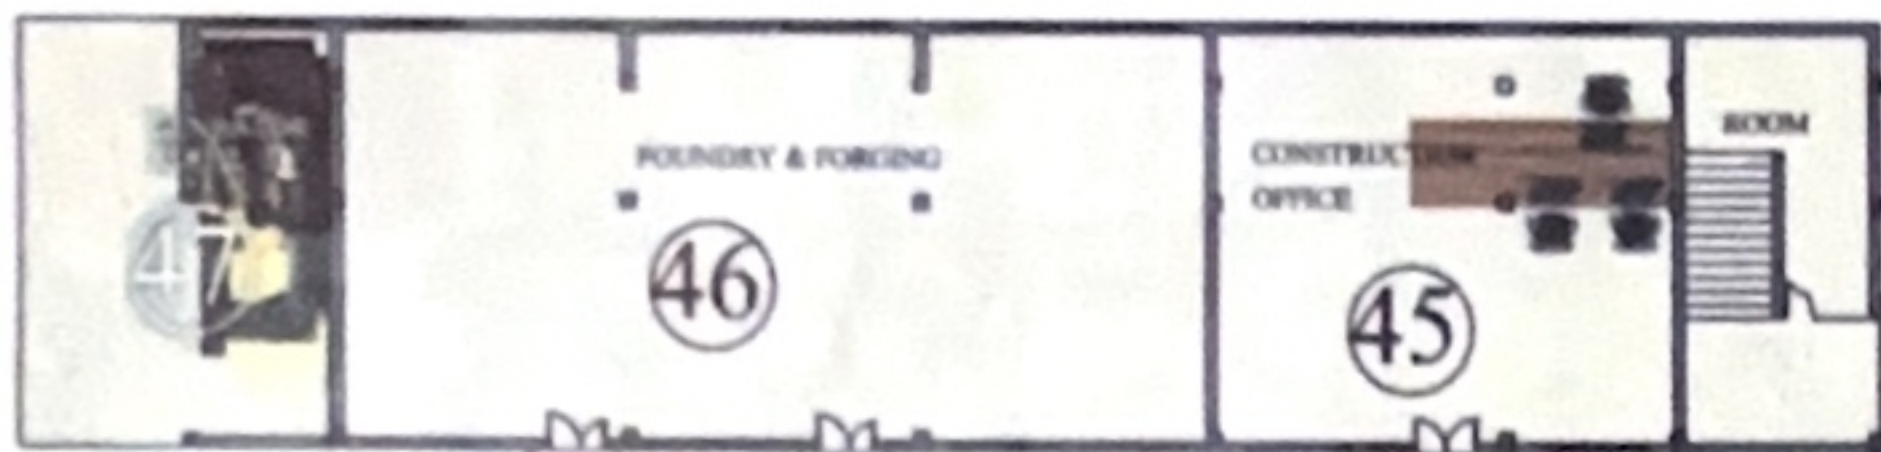

GROUND FLOOR


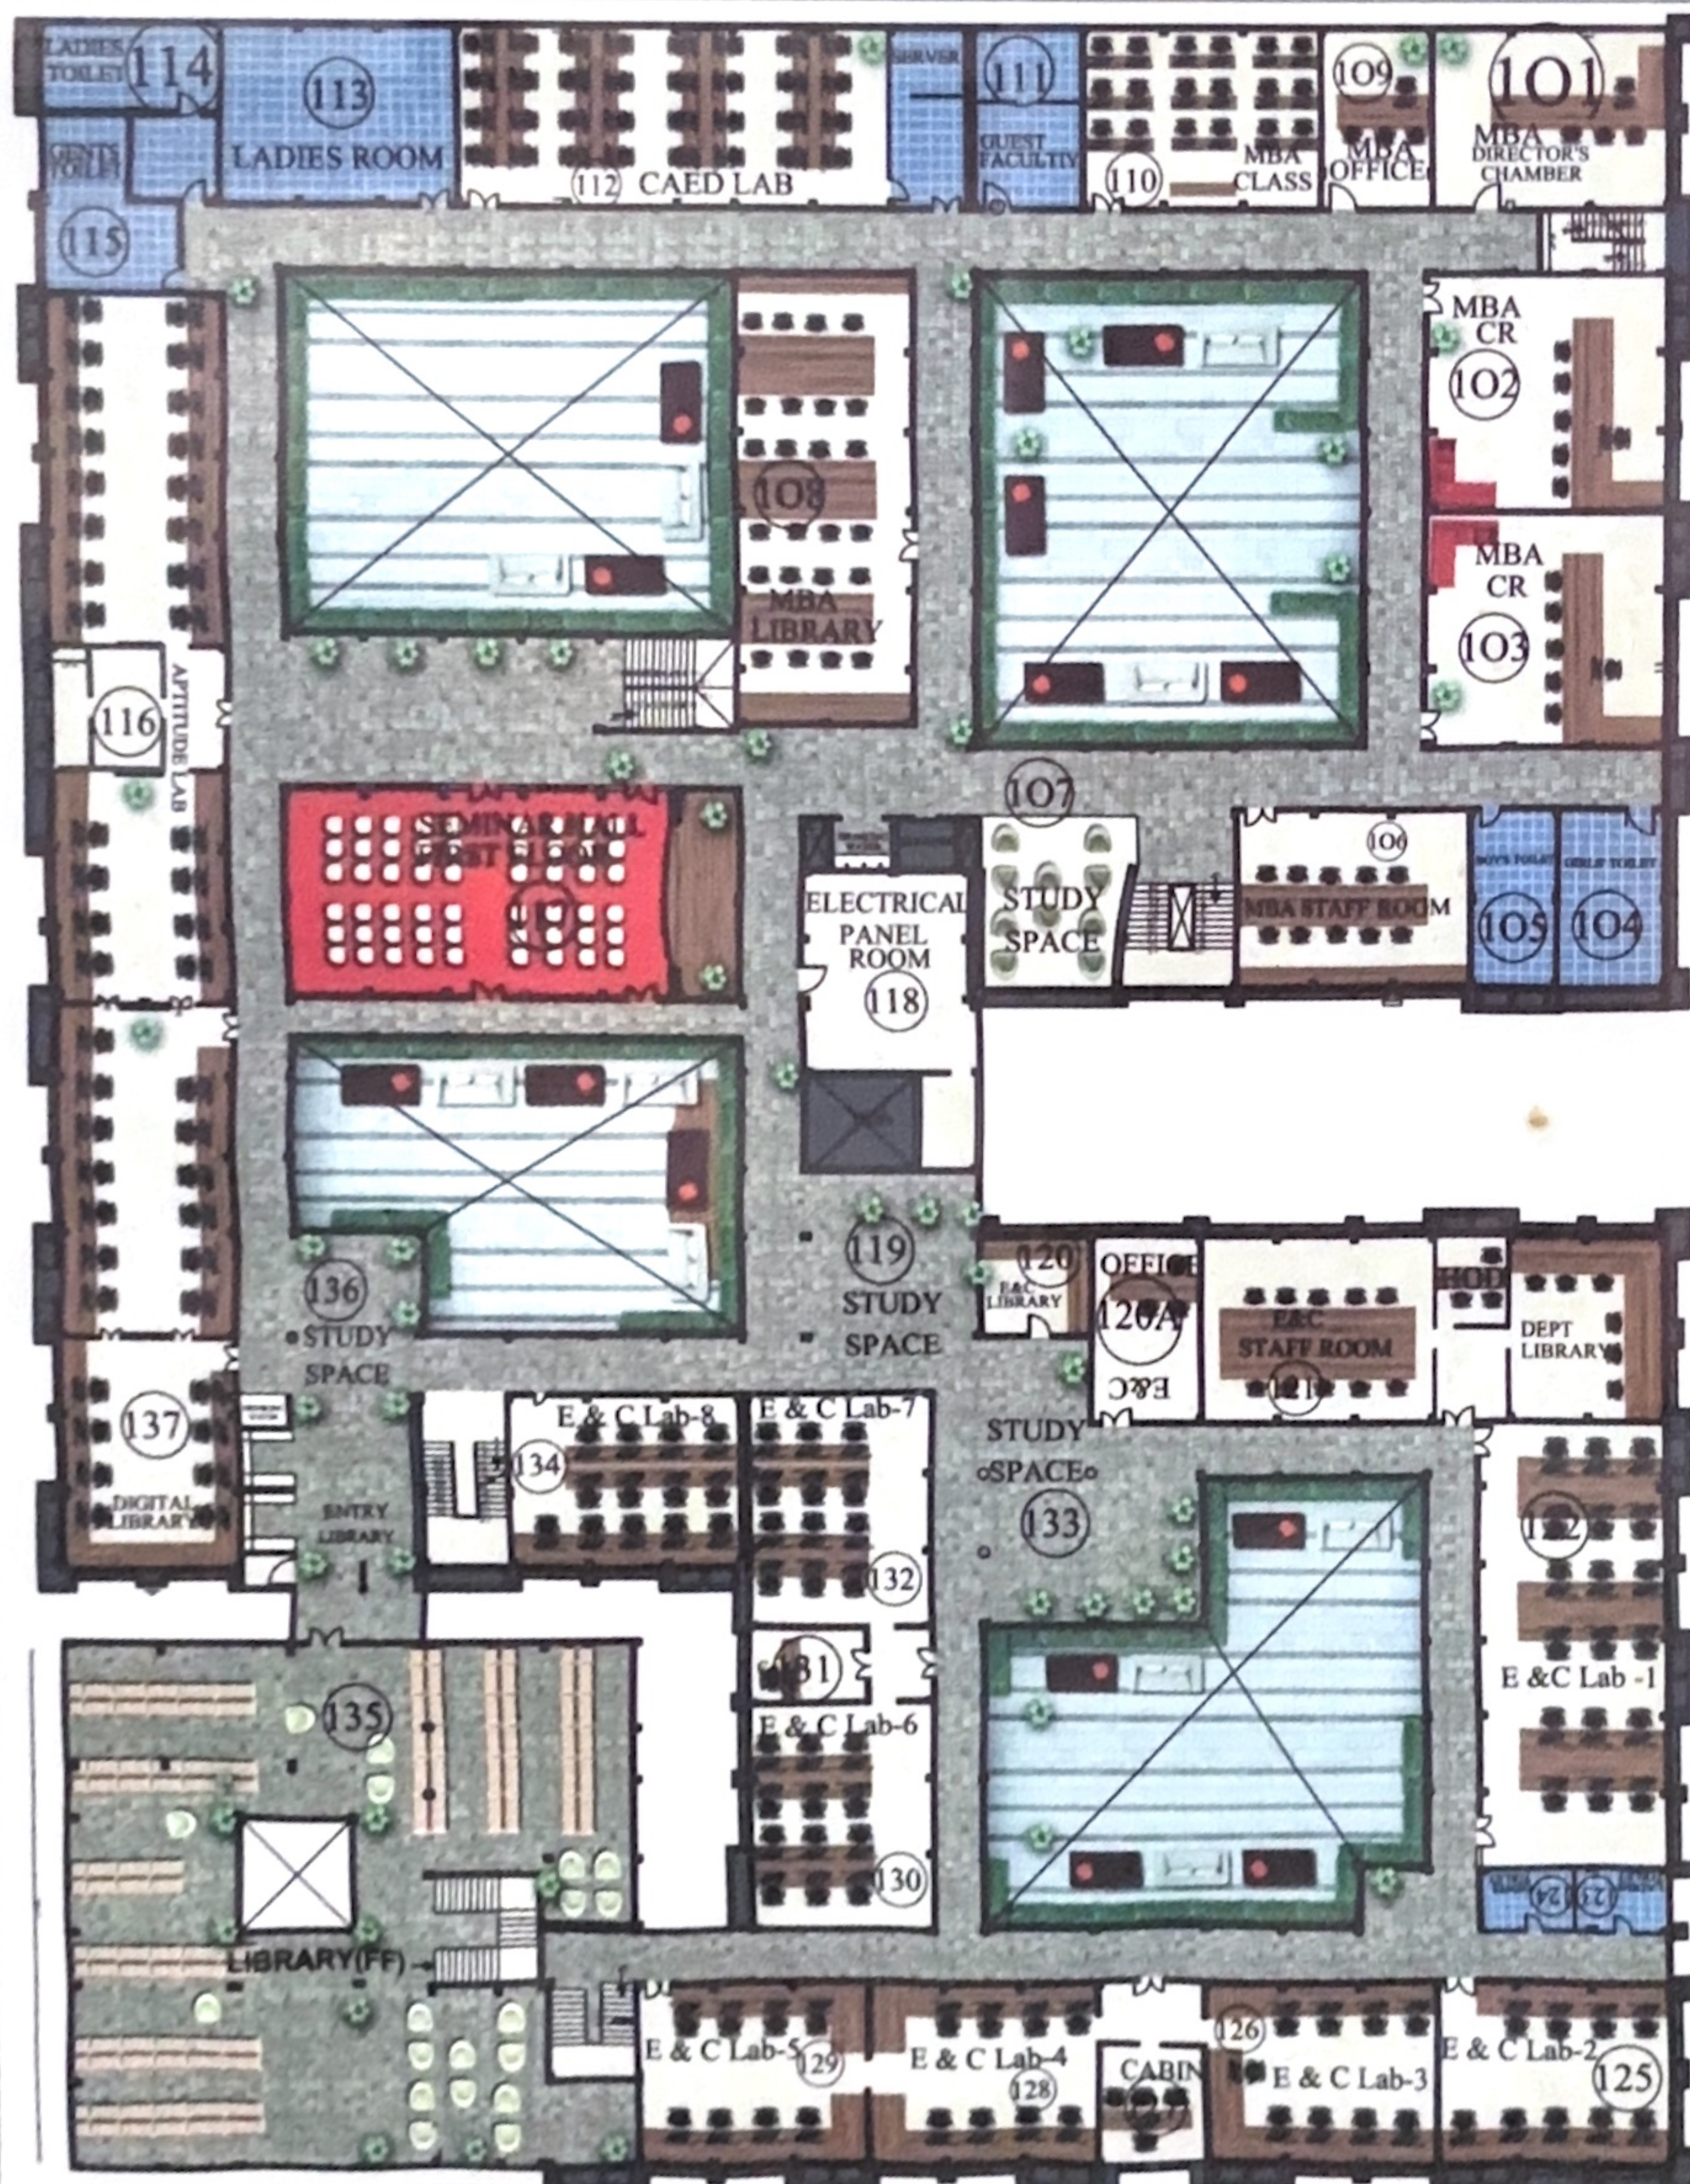


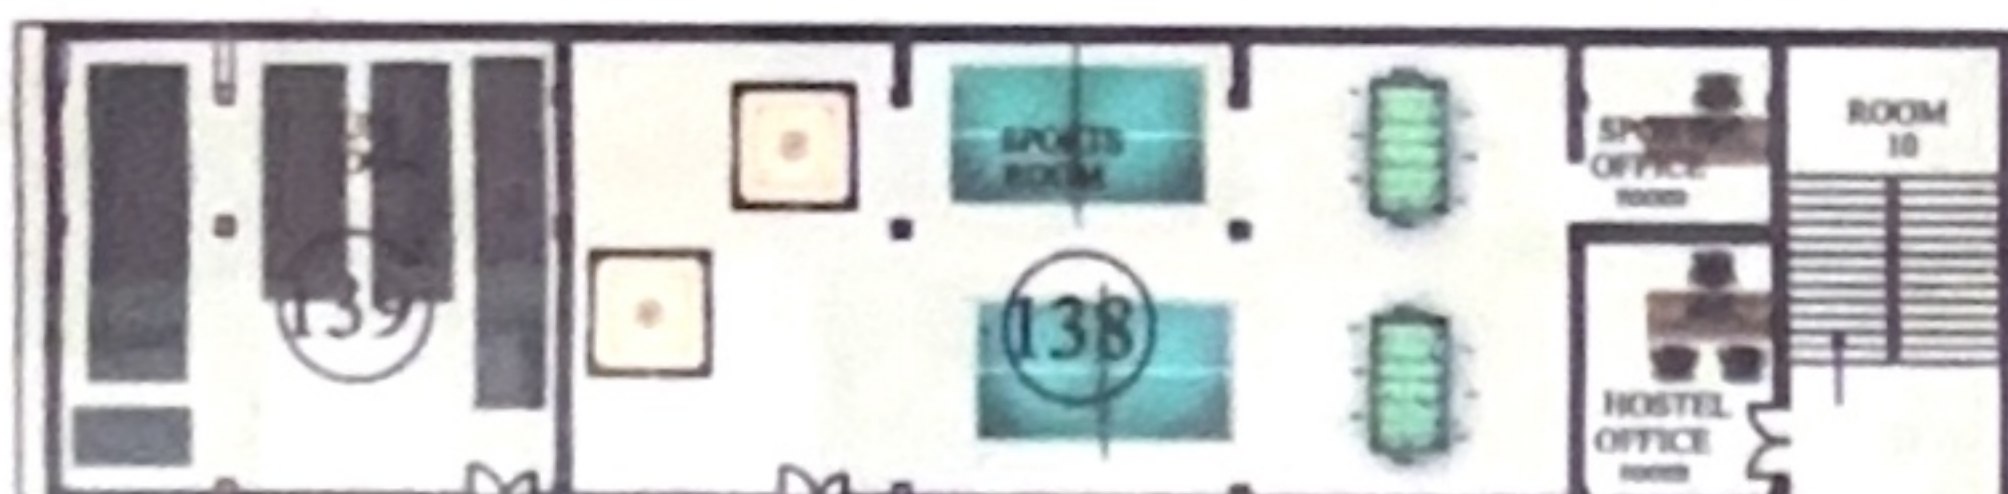

FIRST FLOOR



WORKSHOP SECOND FLOOR

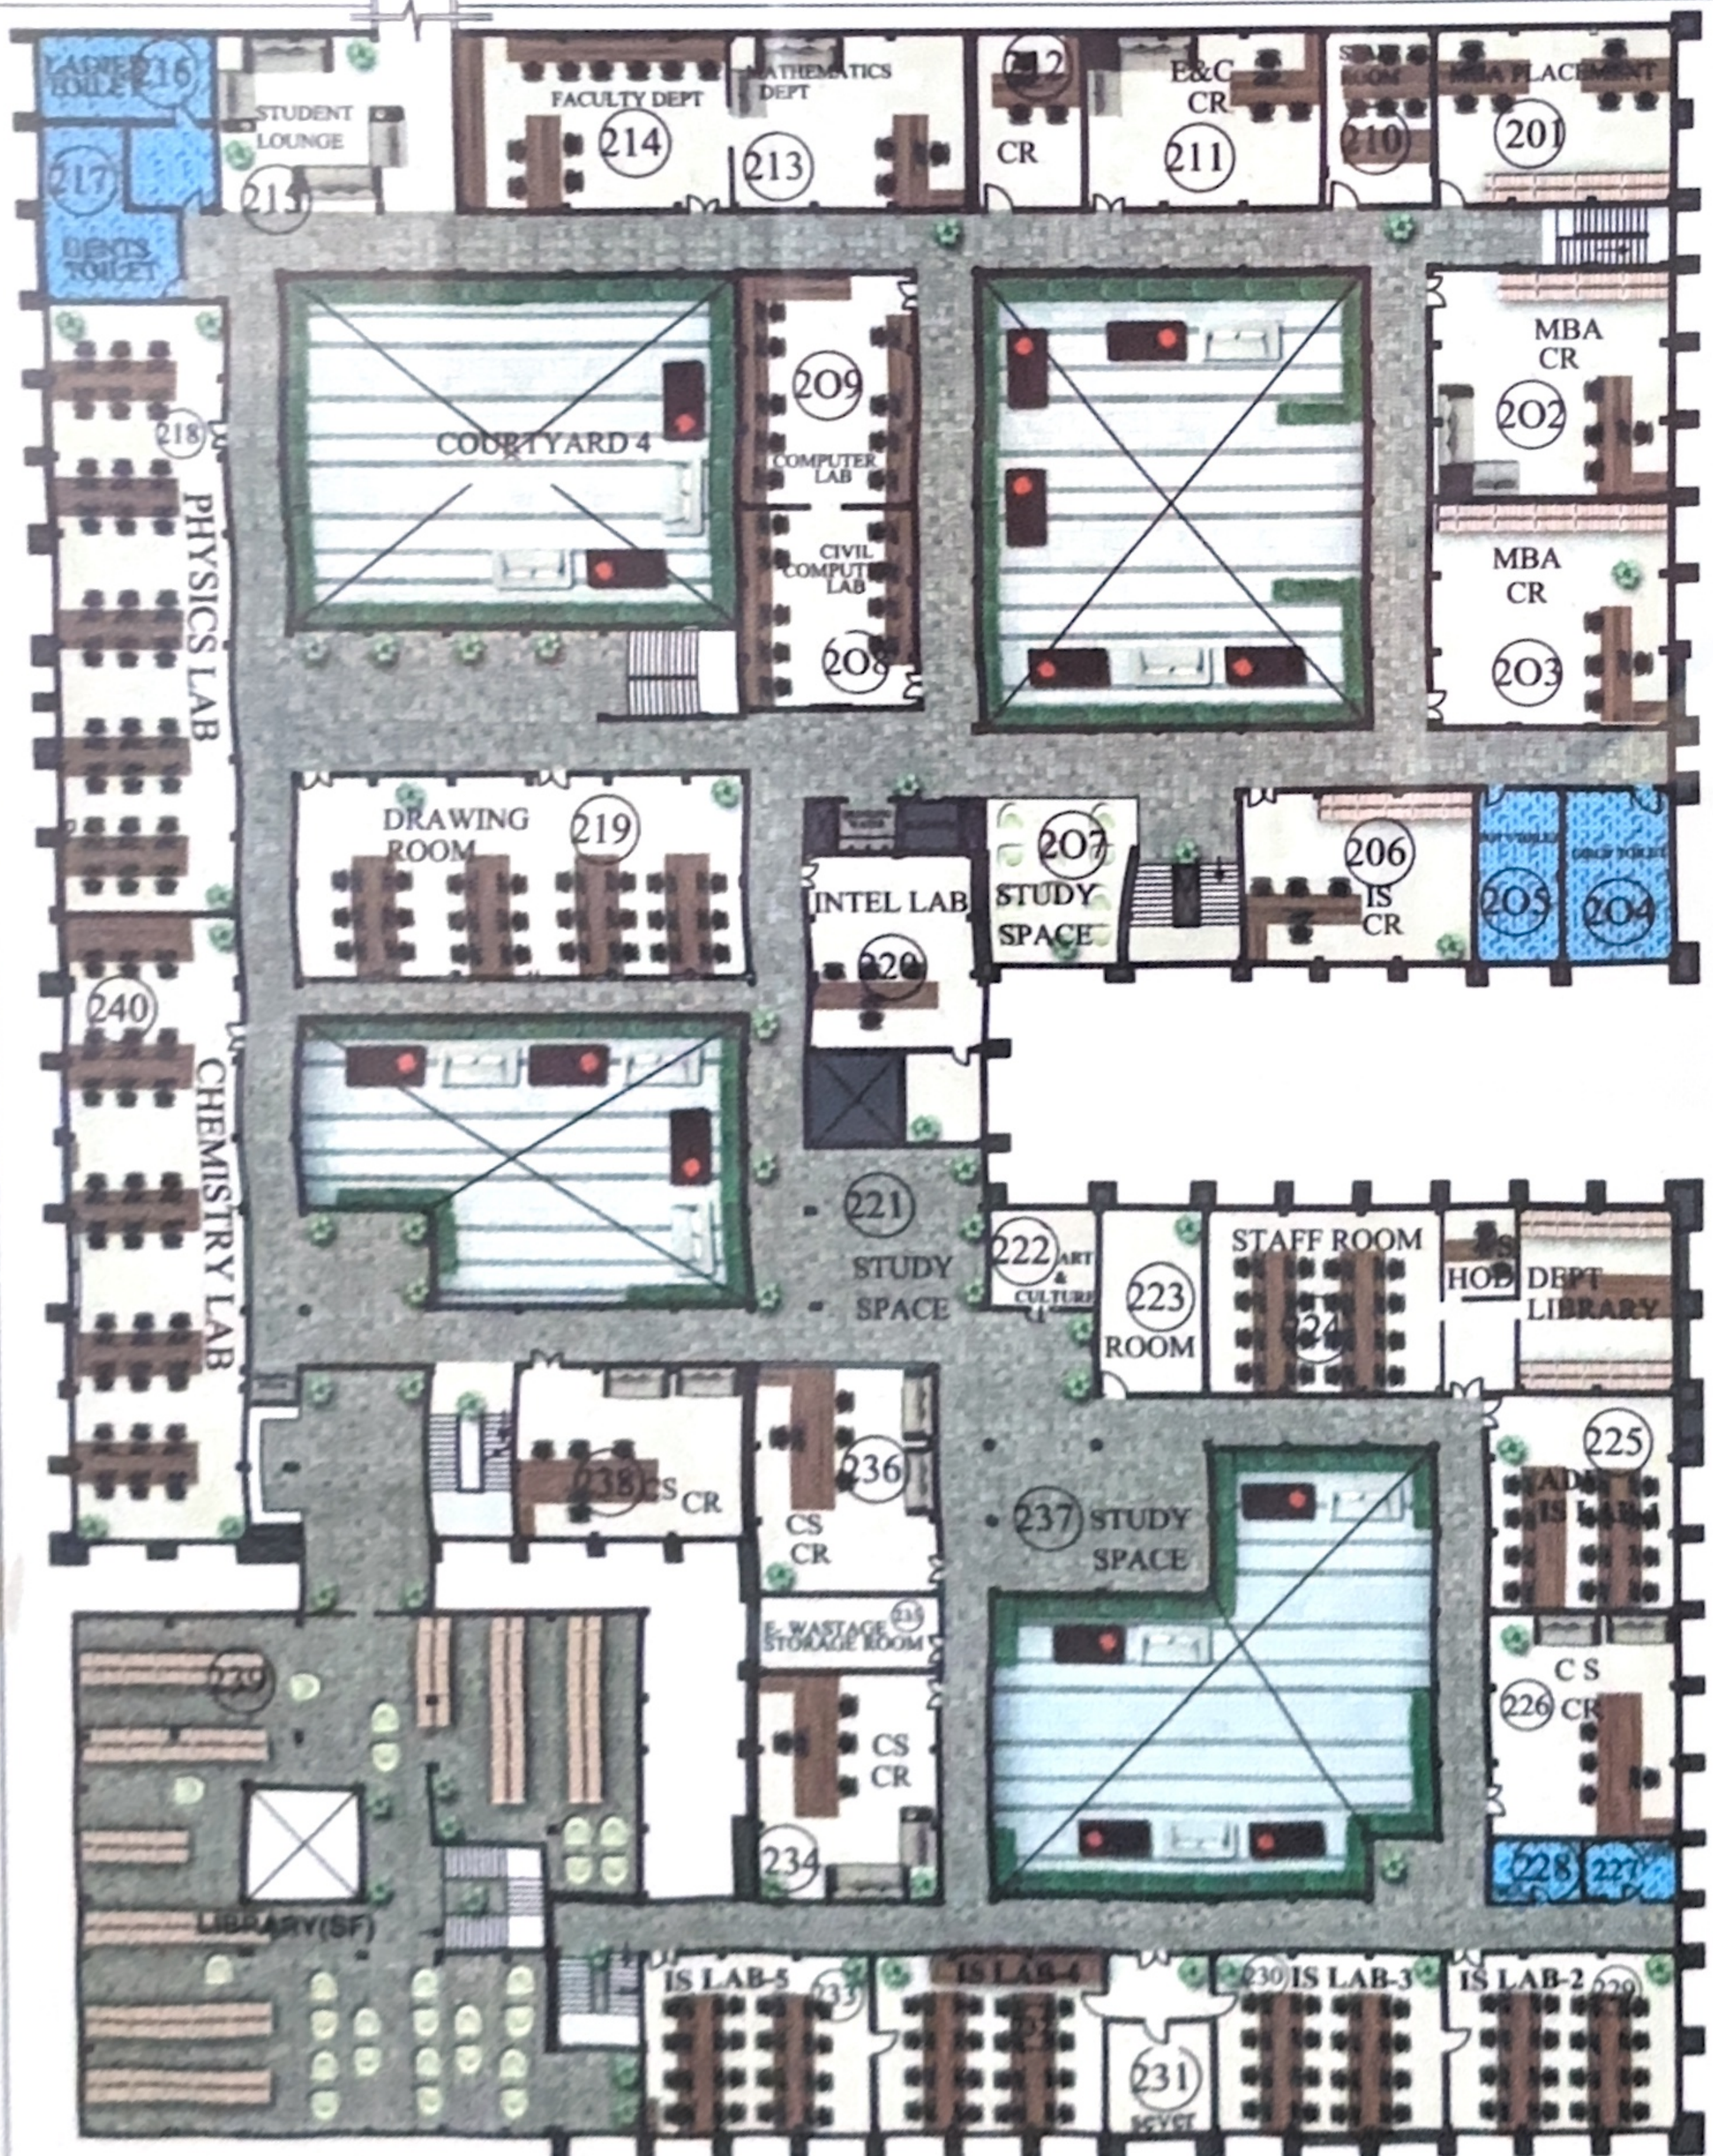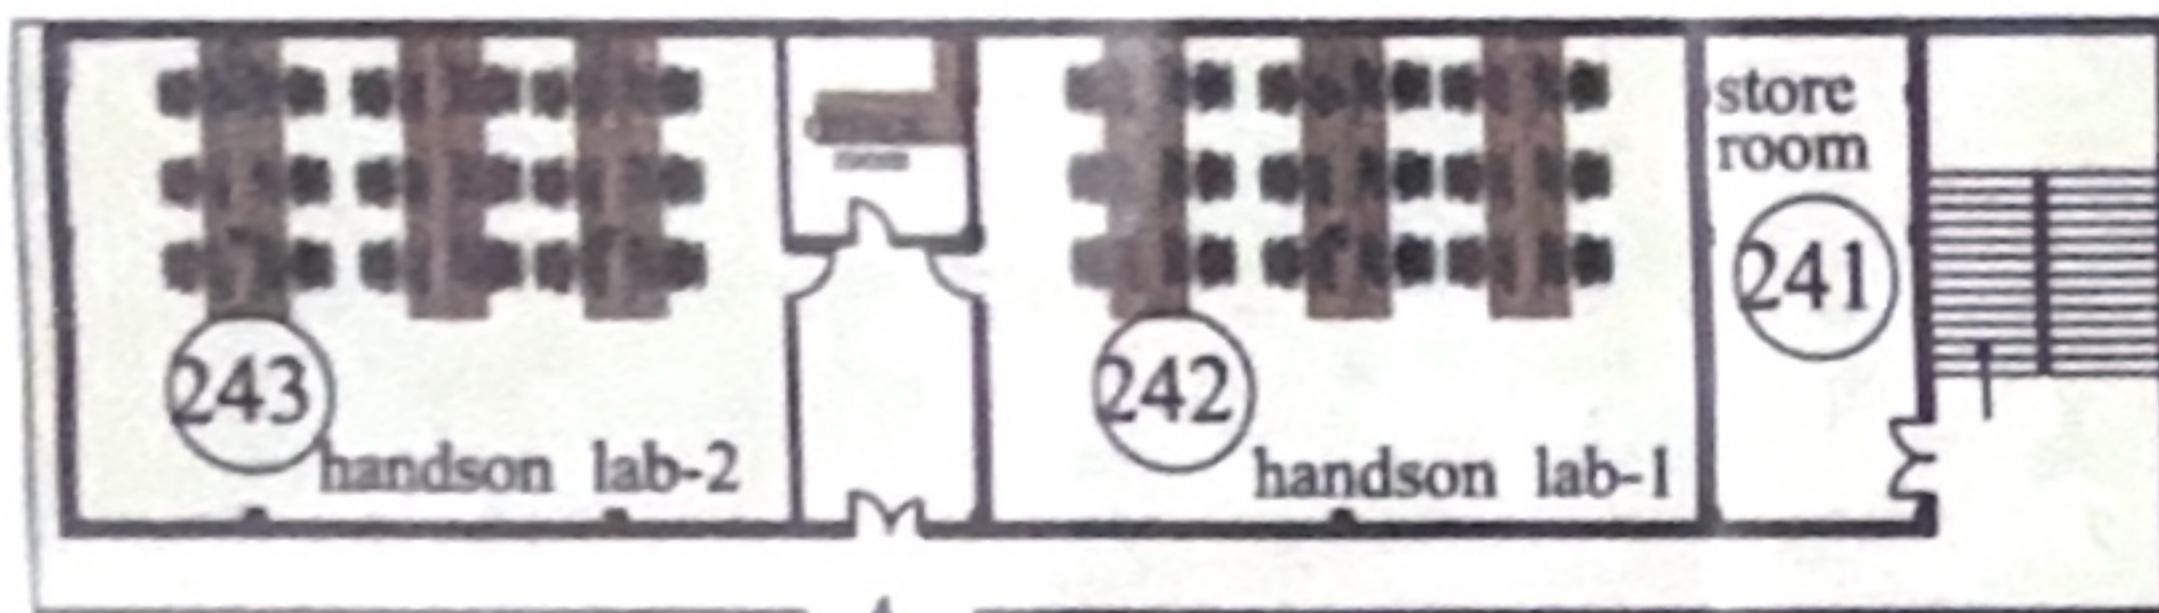

SECOND FLOOR








FIFTH FLOOR




WORKSHOP FOURTH FLOOR

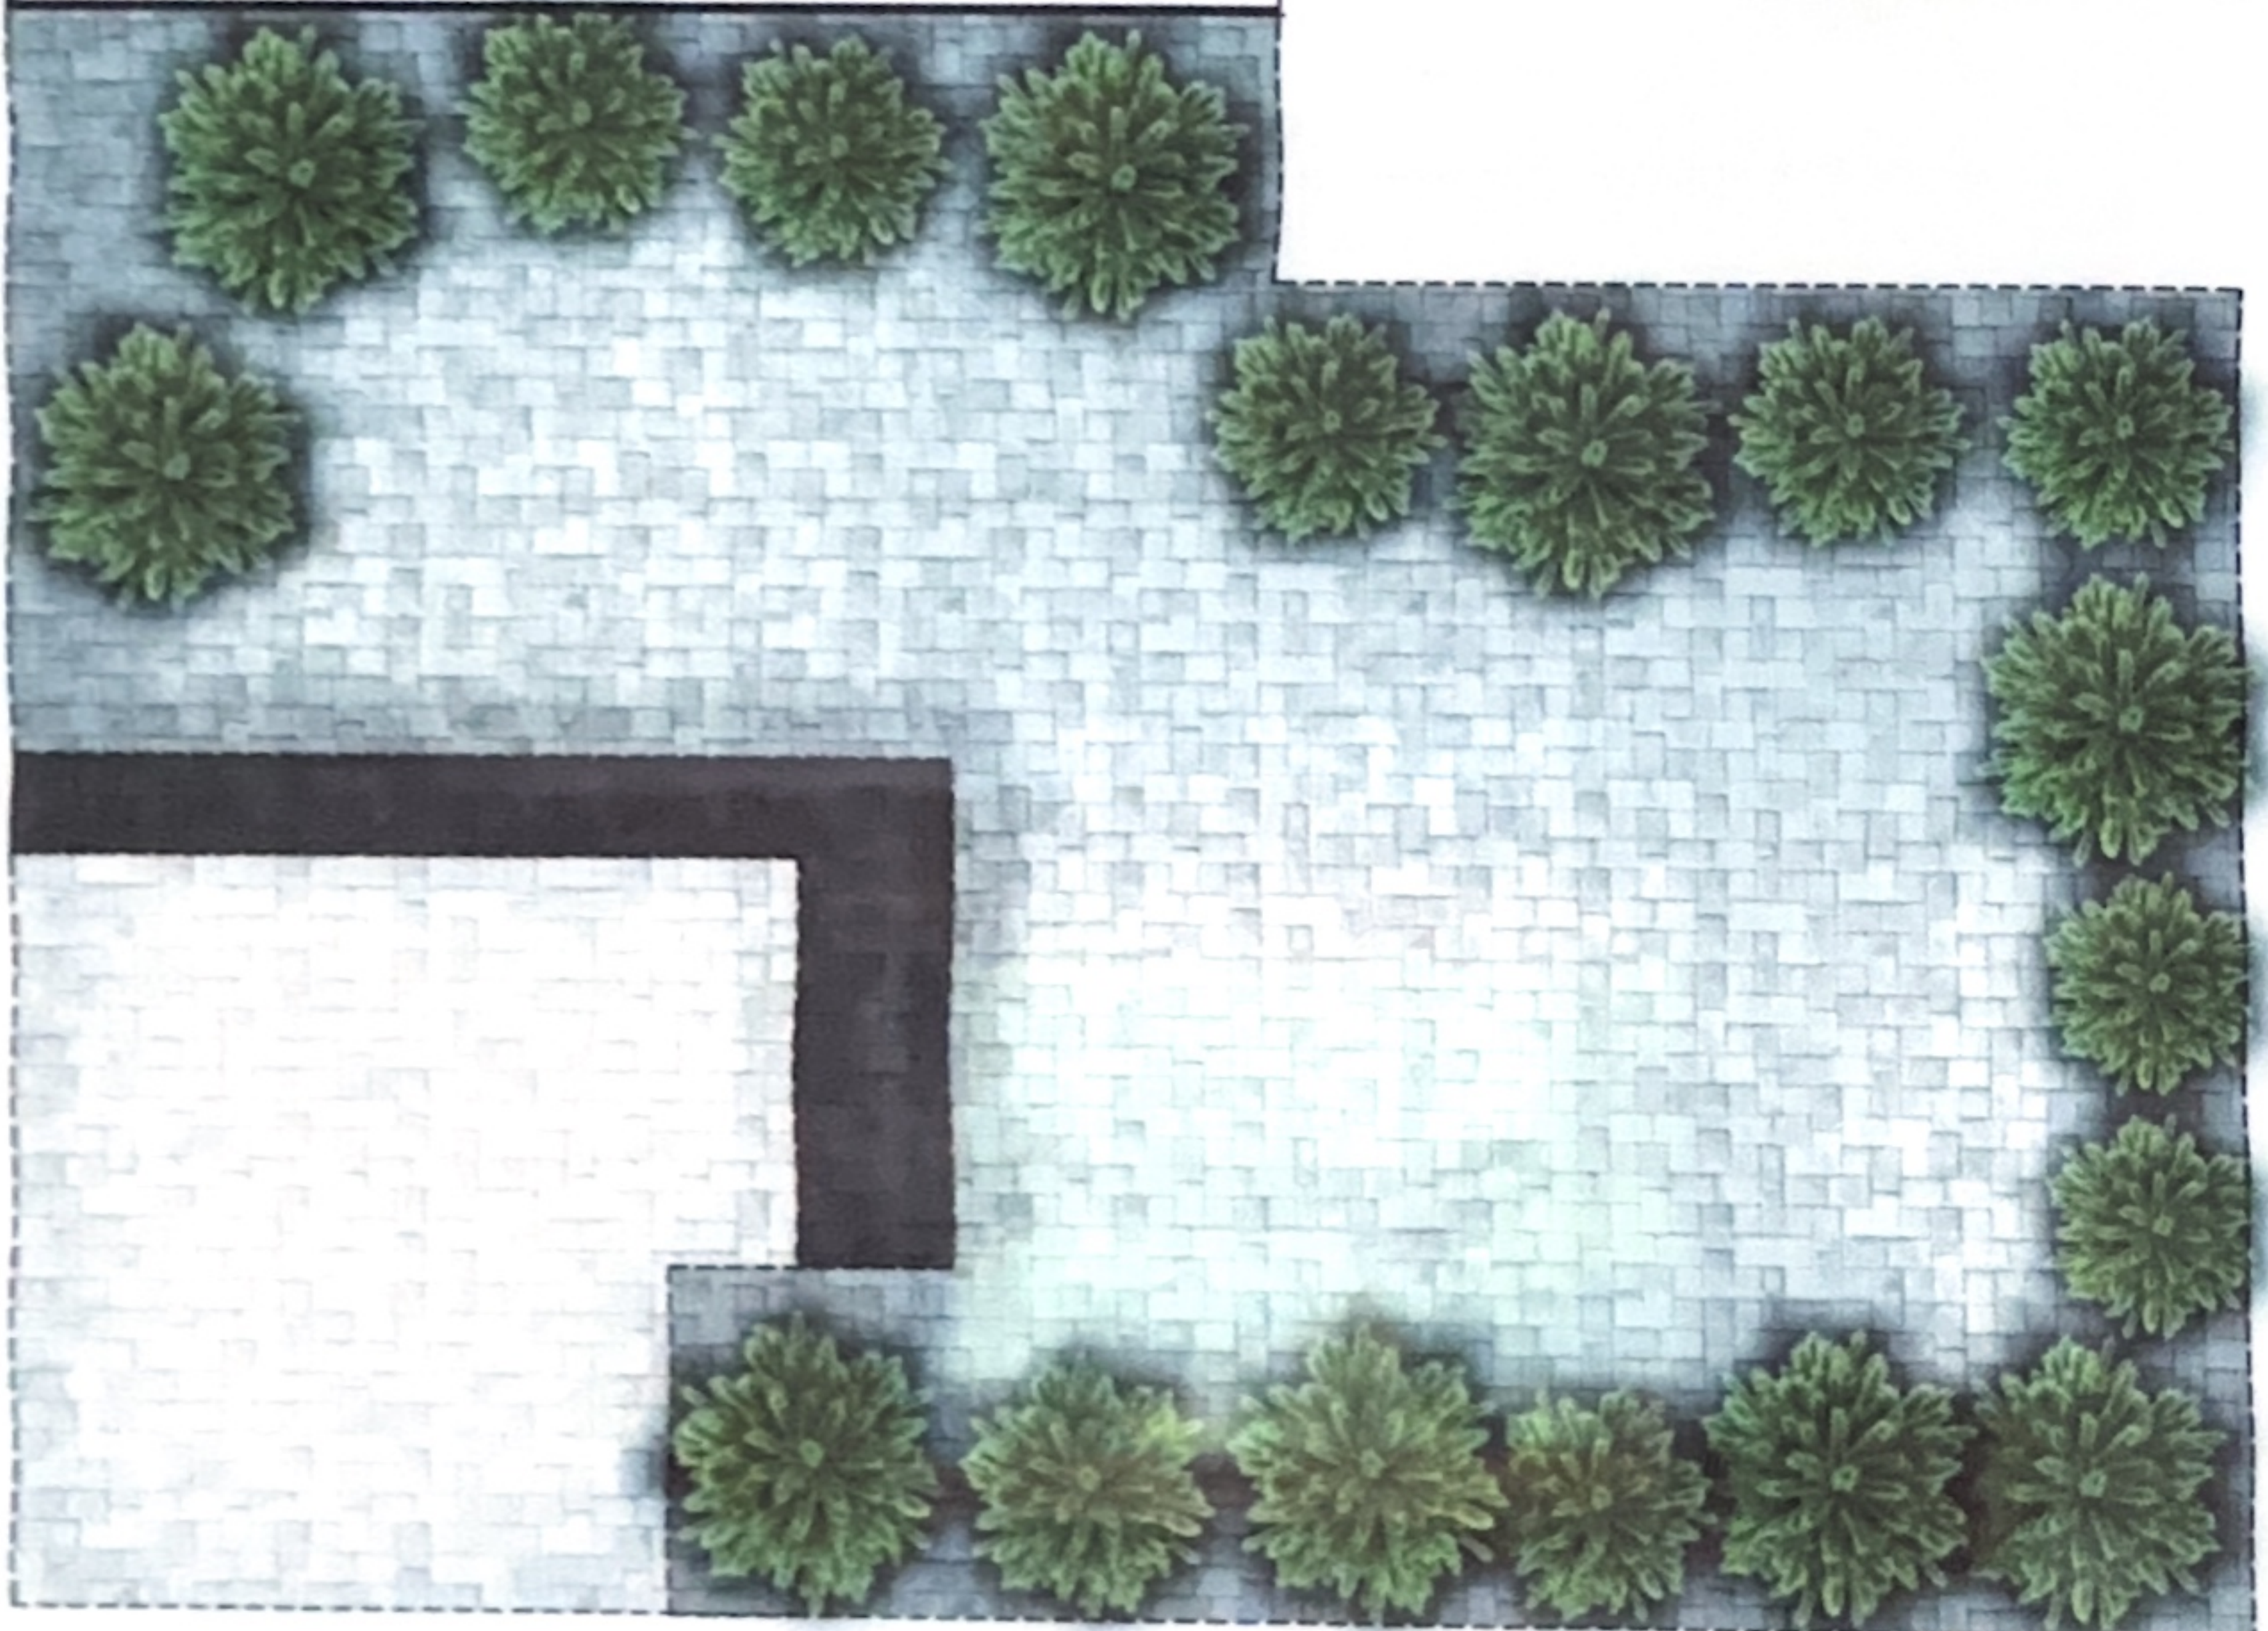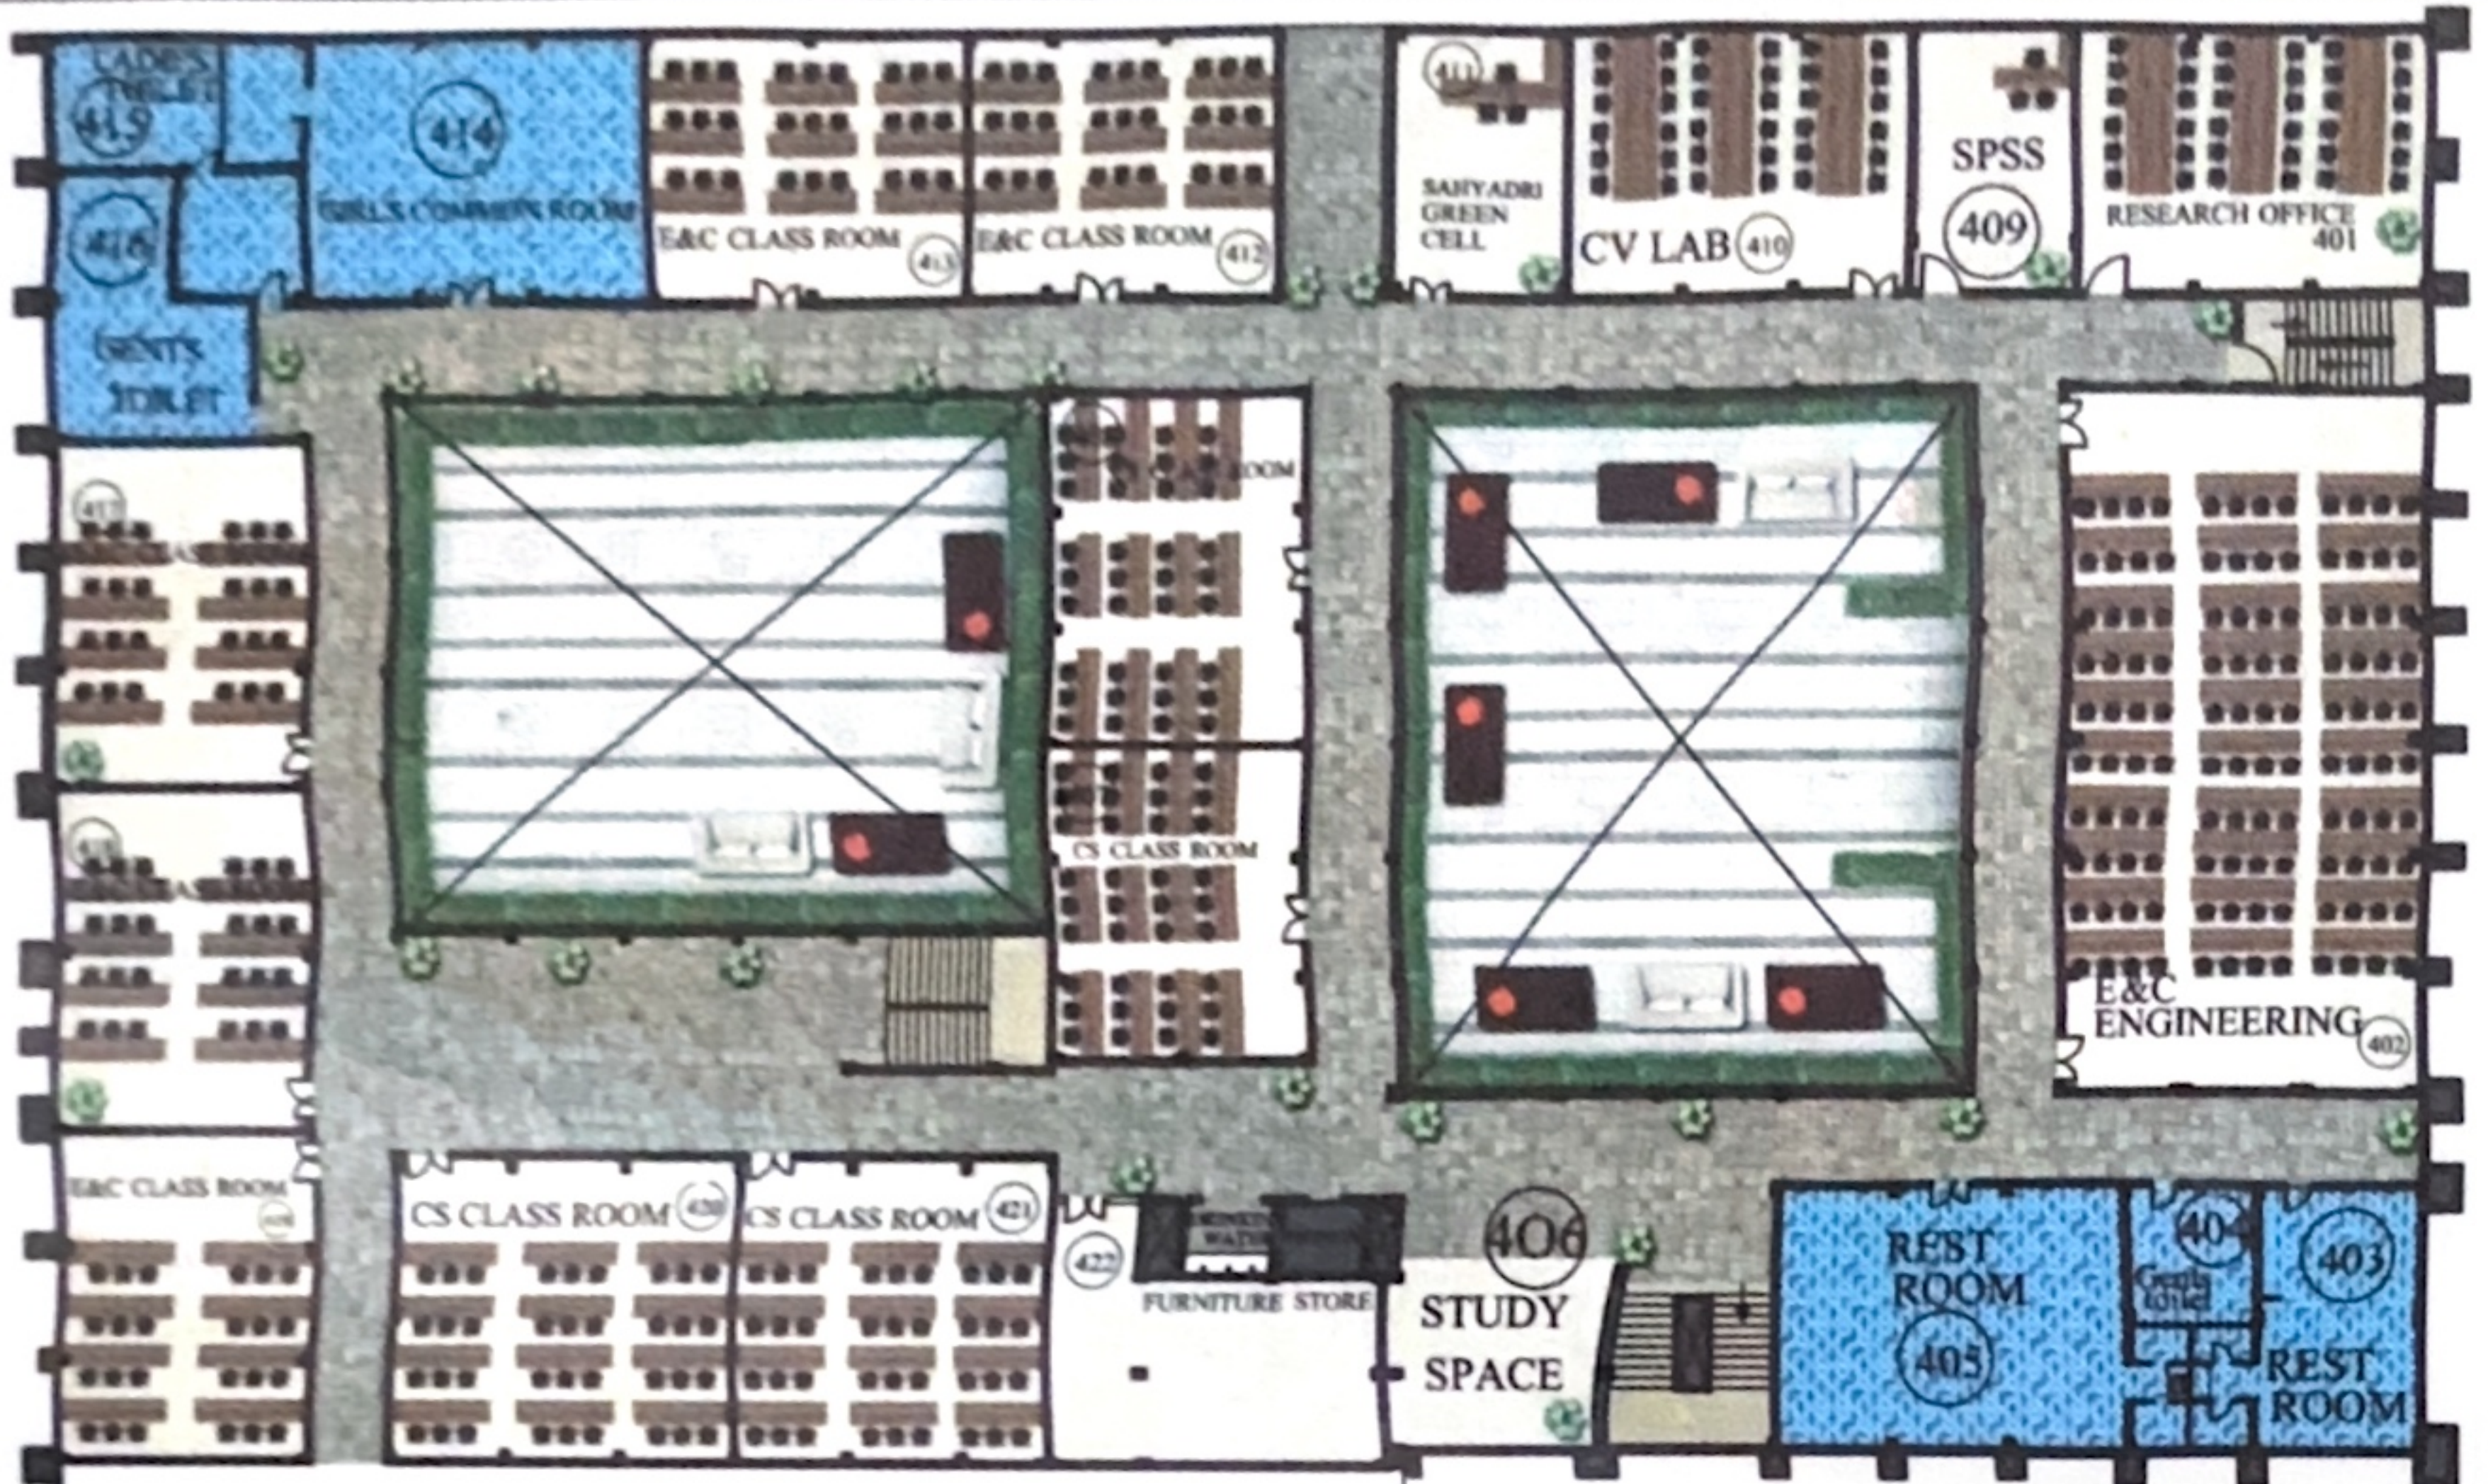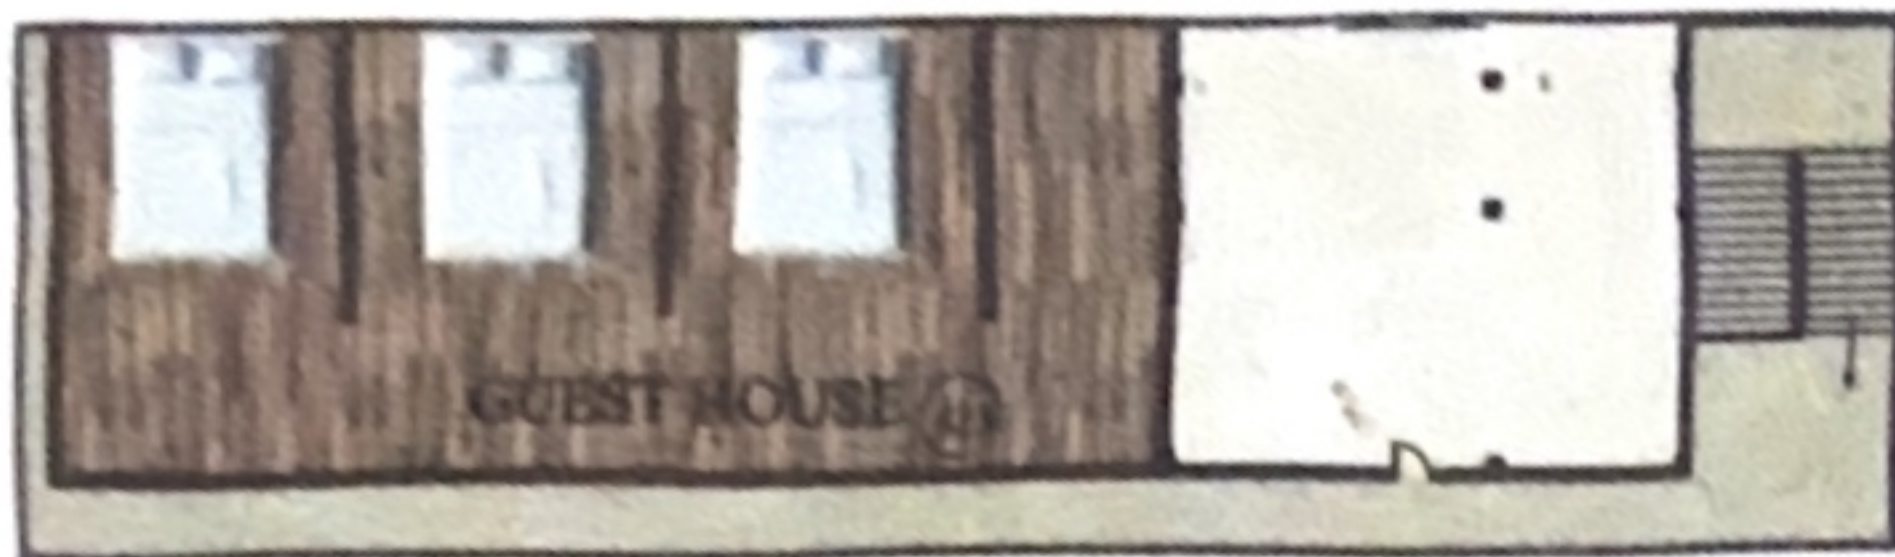

FOURTH FLOOR



WORKSHOP THIRD FLOOR

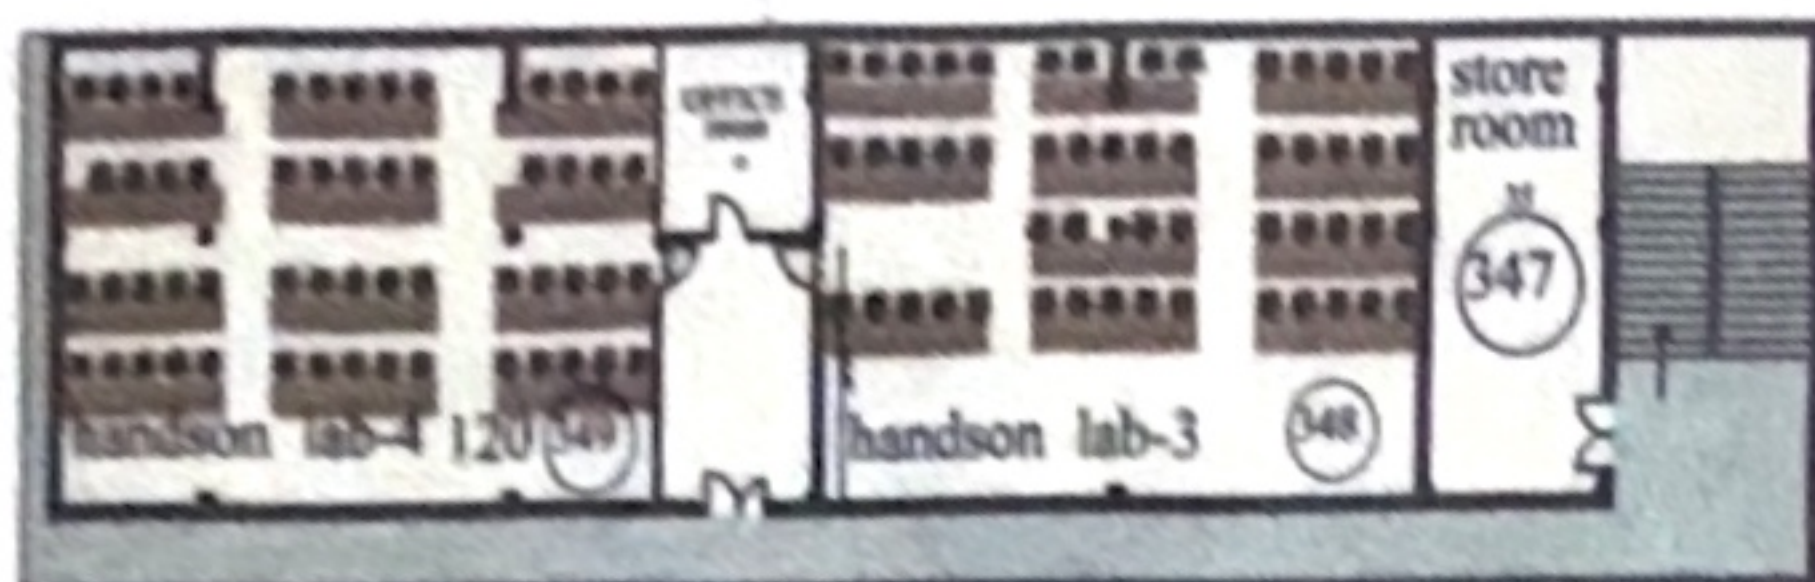

THIRD FLOOR

